


建筑		给排水		电气		动力
结构		暖通		电讯		校工

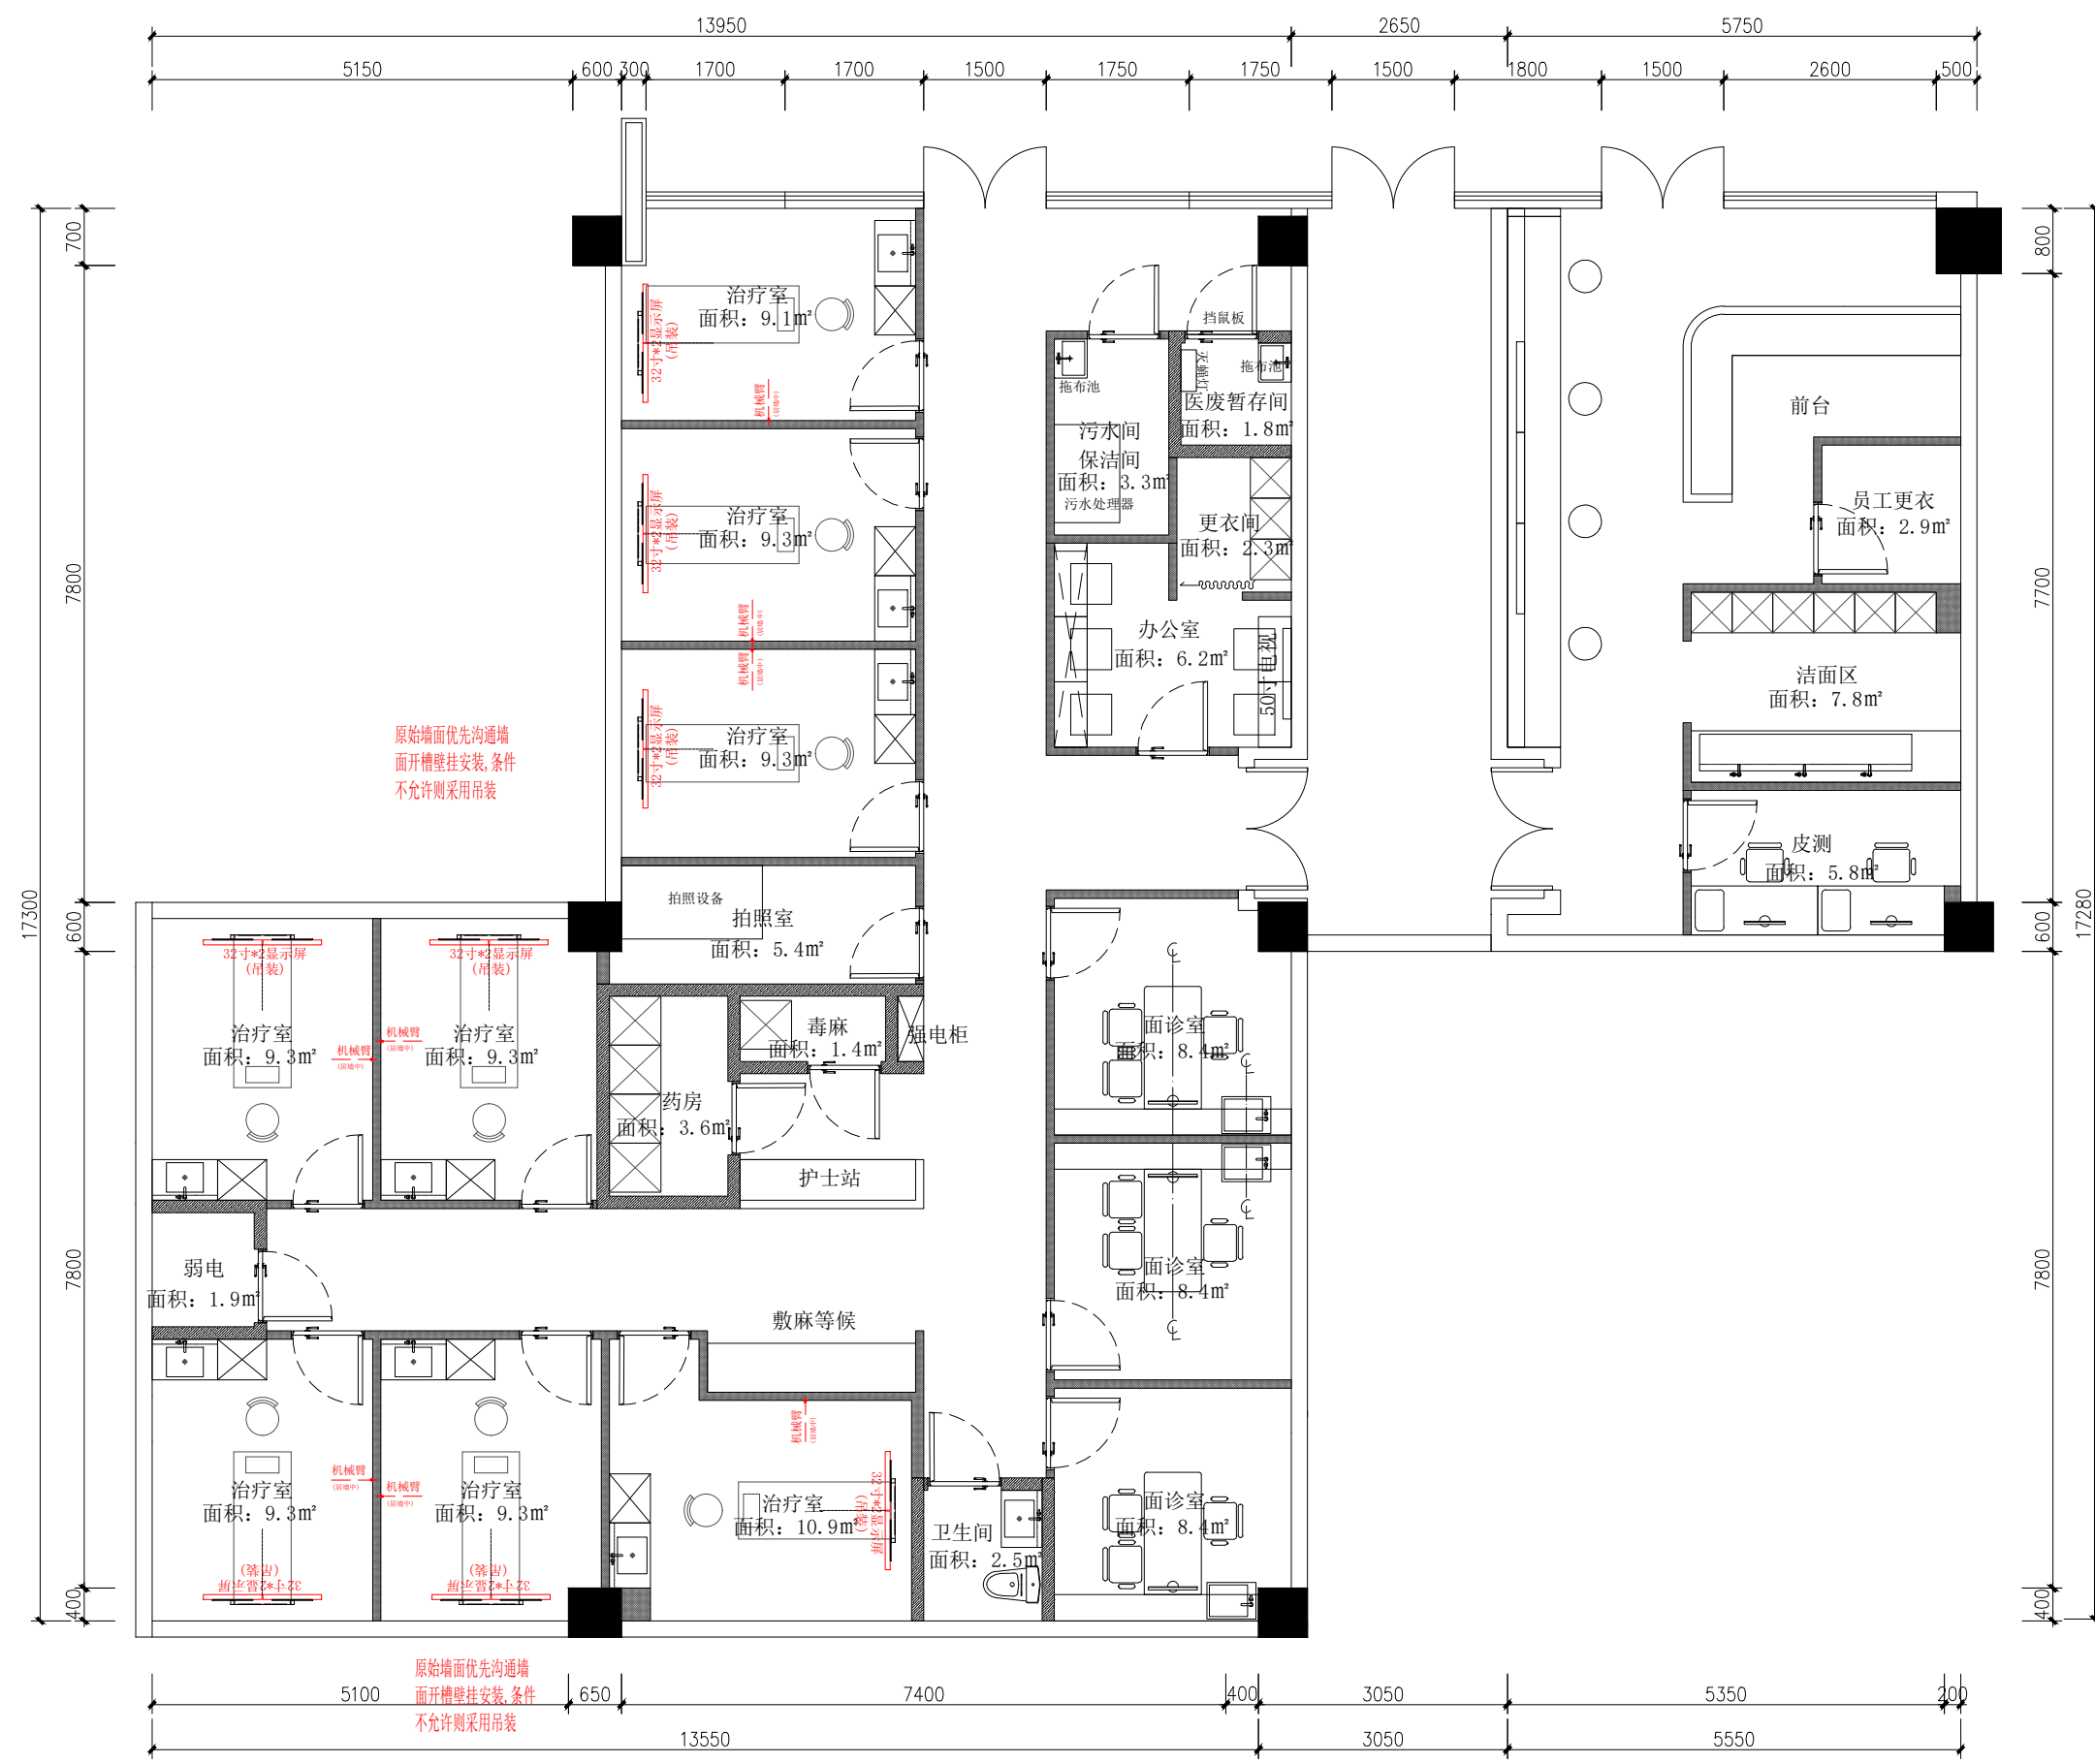

FIXTURE/FURNISHING PLAN

平面布置图

SCALE 1:65

治疗室数量：8间



DESIGN FIRM	???位
-------------	------

COOPERATIVE DESIGN 合作??

CLIENT 建??位

建设单位

PROJECT TITLE	项目名称
---------------	------

新氧青春诊所 深圳壹方城项目 平面系统图

DRAWING TITLE 图名

平面布置图

REVISONS	版本
第一版	2025. 02. 13
第二版	-
第三版	-
第四版	-
第五版	-
第六版	-
APPROVED	
? 定	
VERIFEID	
? 核	
CHECKED	
校 ?	
DESIGNER	
? ?	
DRAWN	
制 ?	
SCALE	
比 例	1 : 65
DATE	
日 期	2025. 02. 13

版权所有
施工时须以标注尺寸为准
施工单位须现场校验尺寸
如有不符须立即通知设计单位
This drawing is copyright
Contractors shall work to the dimensions shown
Contractors must check all dimensions on site
Contractors must be reported immediately in writing

KEY PLAN 索引图

SHEET No. 图号

PL-02

PROJECT No. 项目编号